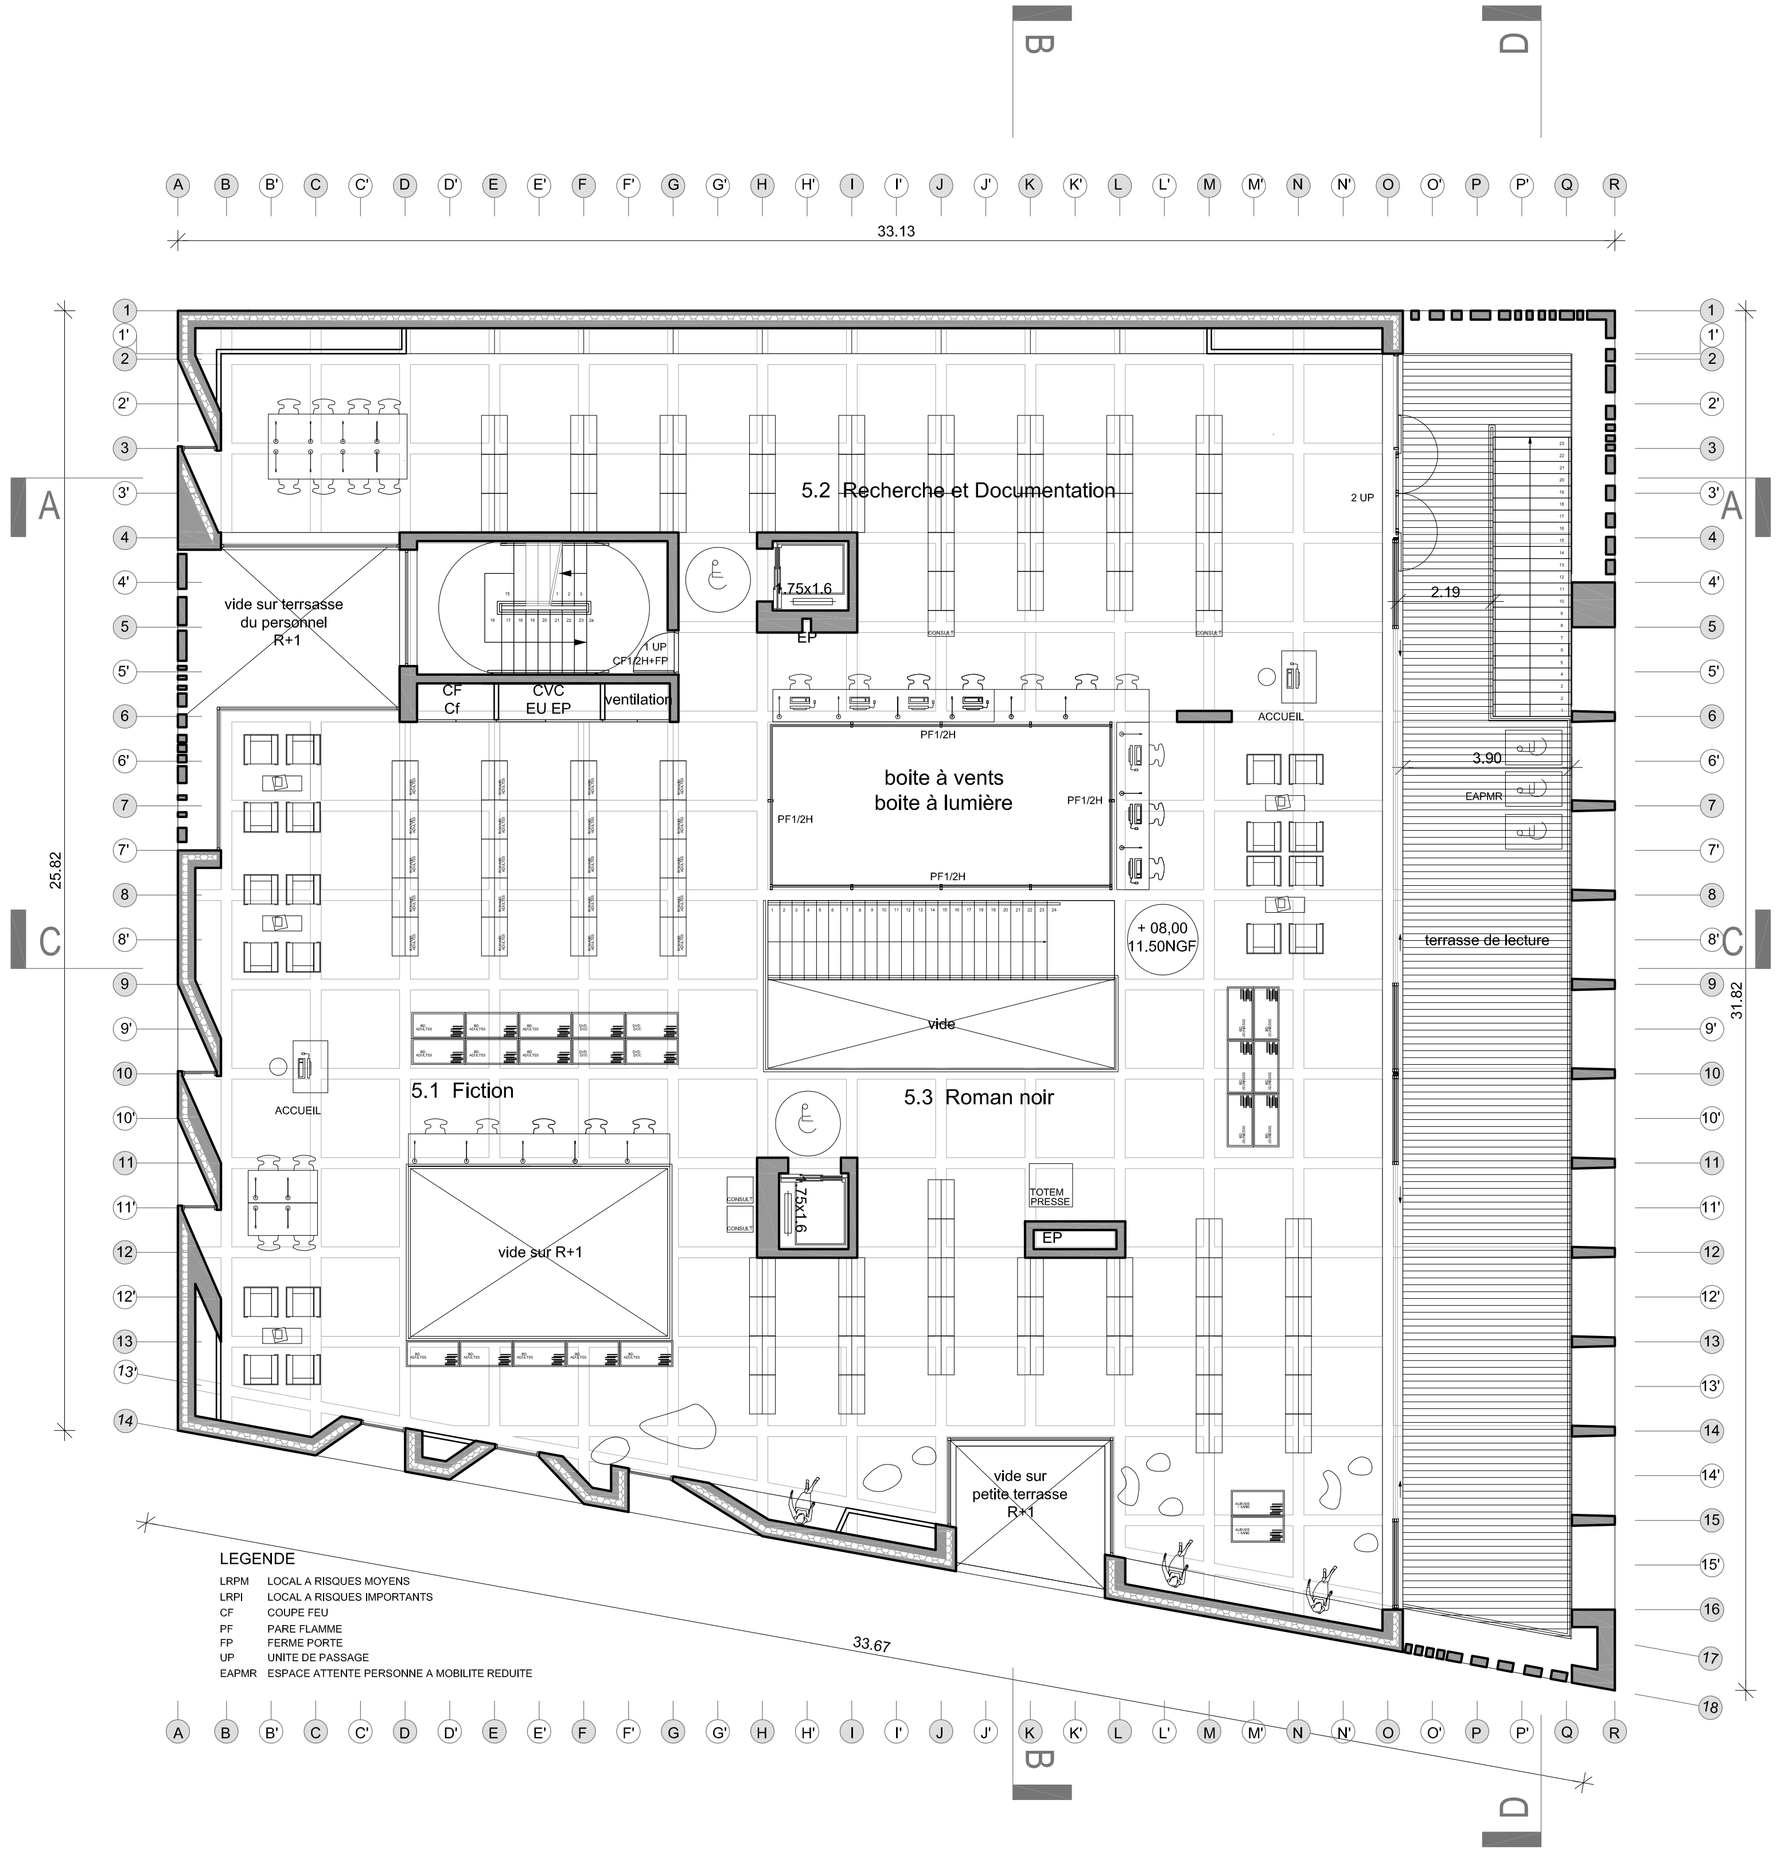


MEDIATHEQUE INTERCOMMUNALE DE FRONTIGNAN-LA-PEYRADE- LOT E1- ZAC DES PIELLES

MAITRISE D'OUVRAGE

MAITRISE D'OUVRAGE : THAU AGGLO
4, avenue d'Algues BP 600
34110 Frontignan cedex
Tel: 04 67 46 47 11
Fax: 04 67 46 47 03

AMO HQE : AUBAINE
13 Bd St Louis BP 28
34150 Guignac
Tel: 04 67 57 80 58
Fax:04 67 57 79 49

BUREAU DE CONTROLE : APAVE
Espace Jean Moulin
44, Avenue Jean Moulin
34500 BEZIERS
Tél. 04 67 35 90 84 Fax. 04 67 35 29 18
Portable : 06 19 73 49 17
dominique.cussac@apave.com

BUREAU DE CONTROLE : APAVE
Espace Jean Moulin
44, Avenue Jean Moulin
34500 BEZIERS
Tél. 04 67 35 90 84 Fax. 04 67 35 29 18
Portable : 06 19 73 49 17
dominique.cussac@apave.com

DATE INDICE

MAITRISE D'OEUVRE

MANDATAIRES
TAUTEM ARCHITECTURE: D. DELORD- J GARCIN
14 Bd Gambetta
30 000 Nîmes.
Tel: 04 66 21 13 49
Fax:
tautem@wanadoo.fr

BMC ARCHITECTES : A. BICAL et L. COURCIER
15 rue Martel.
75010 PARIS
Tel: 01 53 34 03 36
Fax: 01 53 34 03 38
email: frontignan@bmc2.fr

ECONOMISTE FLUIDES: INGEFLUX-DGCI
337, Rue de Guyenne.
84100, Orange
Tel: 04 90 51 85 35
Fax:
email: vaucluse@ingeflux-dgci.fr

ACOUSTICIEN : AYDA Ingénieurs-conseils
4 Résidence des Douze Arpents.
78810 FEUCHEROLLES
Tel/Fax: 01 30 54 55 73
email: aydeka@orange.fr

BET STRUCTURE : BEST
Chemin de Vaques Basse.
30127 Bellegarde
Tel: 04 66 01 13 56
Fax:
email: charlesportefaix@aol.com

P C	FEVRIER 2012
PLAN NIVEAU2	Ech : 1/100
	ARCHI
PC-PLANSARCHI.dwg	05